

A series of thin, green, wavy lines that originate from the top left, curve around the text, and extend towards the bottom right, creating a sense of movement and depth.

Projeto de Arquitetura III

CONDOMÍNIO RESIDENCIAL MAGAL

IASMIN GALVÃO E LETÍCIA MARTINS - 5º P



1 PLANTA DE LOCAÇÃO
ESCALA 1/350




VISTA 1



VISTA 2



VISTA 3

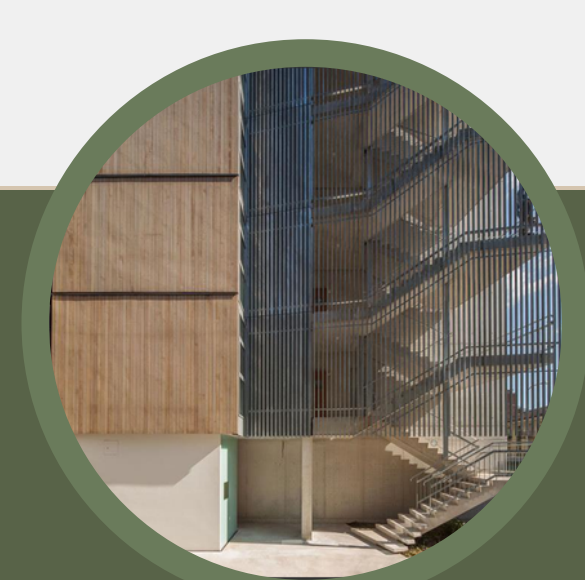


Referência:
Apartamentos em
Lugano SPBR

ESTUDO DO TERRENO E CONTEXTO

O projeto foi desenvolvido para um terreno plano localizado no bairro Aero Clube, em Volta Redonda (RJ), uma região com perfil residencial tranquilo, boa infraestrutura urbana e proximidade com comércios, serviços e áreas de lazer, como o parque e o Rio Paraíba do Sul. A vista para o rio e para o verde ao redor foi valorizada desde a concepção da proposta.

ÍNDICES URBANÍSTICOS


Área: 4.913,79m²
Coeficiente de aproveitamento: 4 - Decreto 13.074
Potencial construtivo: 19.655,16m²
Taxa de ocupação: 70% - Decreto 1412 -1977
Afastamento Frontal: 3,00m
Afastamento Lateral: 1,50m Zona: ZH1

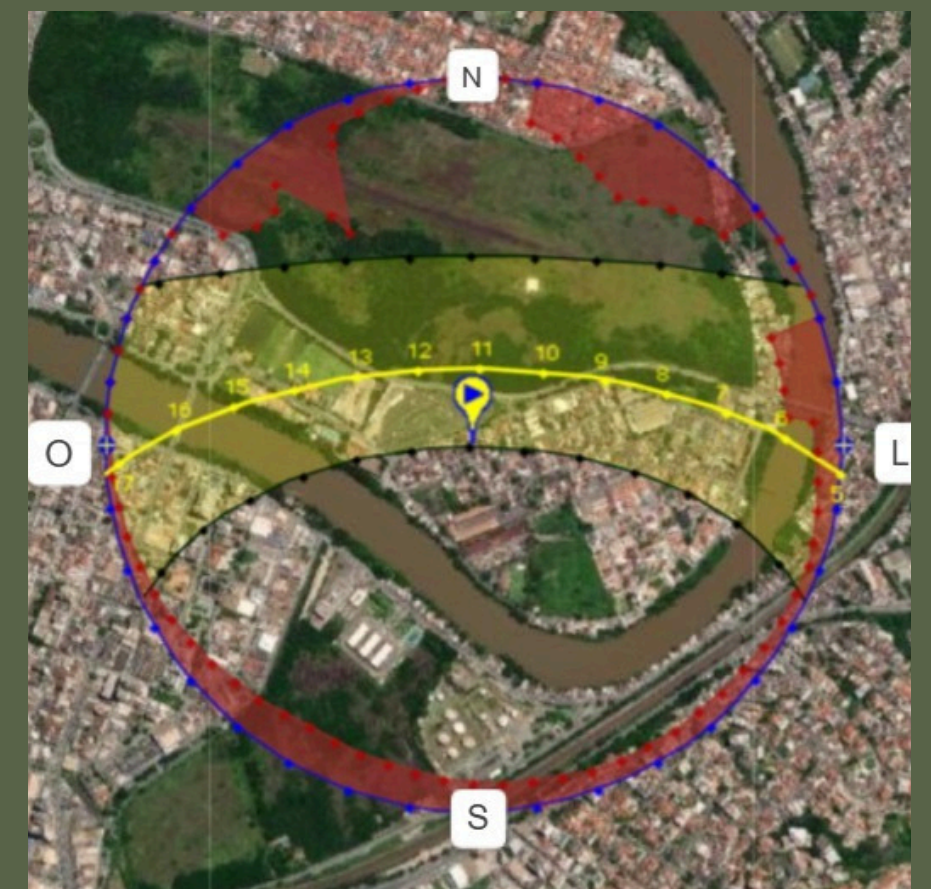

PROJETO:		PROJETO DE ARQUITETURA III	
ALUNAS:		ESTUDO DE IMPLANTAÇÃO	
MATRÍCULAS:		IASMIN GALVÃO E LETÍCIA MARTINS	
MTRÍCULAS:		2023121337 e 2023121779	
ESCALA:		PRANCHA:	
1/350		01/12	
DESENHO:		DATA:	
01/12		03/06/2025	

A análise climática teve papel essencial na implantação. Foram observados fatores como a incidência solar e os ventos predominantes da região, o que permitiu posicionar os edifícios de forma a garantir ventilação cruzada, conforto térmico e iluminação natural nos ambientes internos. A vegetação foi distribuída de forma estratégica para criar sombreamento, melhorar a circulação do ar e aumentar a qualidade ambiental dos espaços externos.

O sistema viário ao redor do terreno, com ruas organizadas e bom fluxo, também influenciou na organização dos acessos. Foram previstas duas entradas de veículos: uma principal com portão e cancela, voltada para a Av. Bartolomeu de Gusmão, e outra, para visitantes, pela Av. Projetada. O acesso de pedestres é único, passando pela guarita e distribuindo o fluxo de forma funcional para todas as áreas comuns, garantindo segurança e controle.

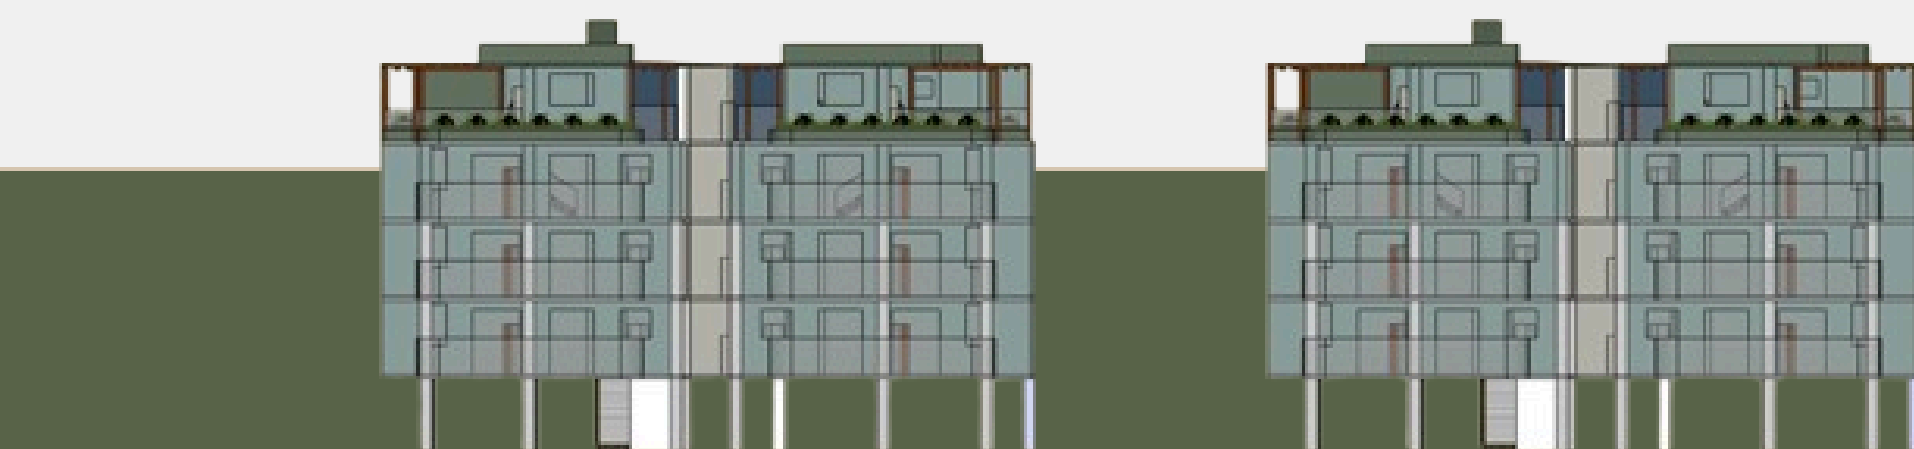

PERFIL ESQUEMÁTICO

ALUNAS: IASMIN GALVÃO E LETÍCIA MARTINS

MATRÍCULAS: 2023121337 e 2023121779


PRANCHA:

ESCALA:
1/250

DESENHO:
02/12

DATA:
03/06/2025


02/12

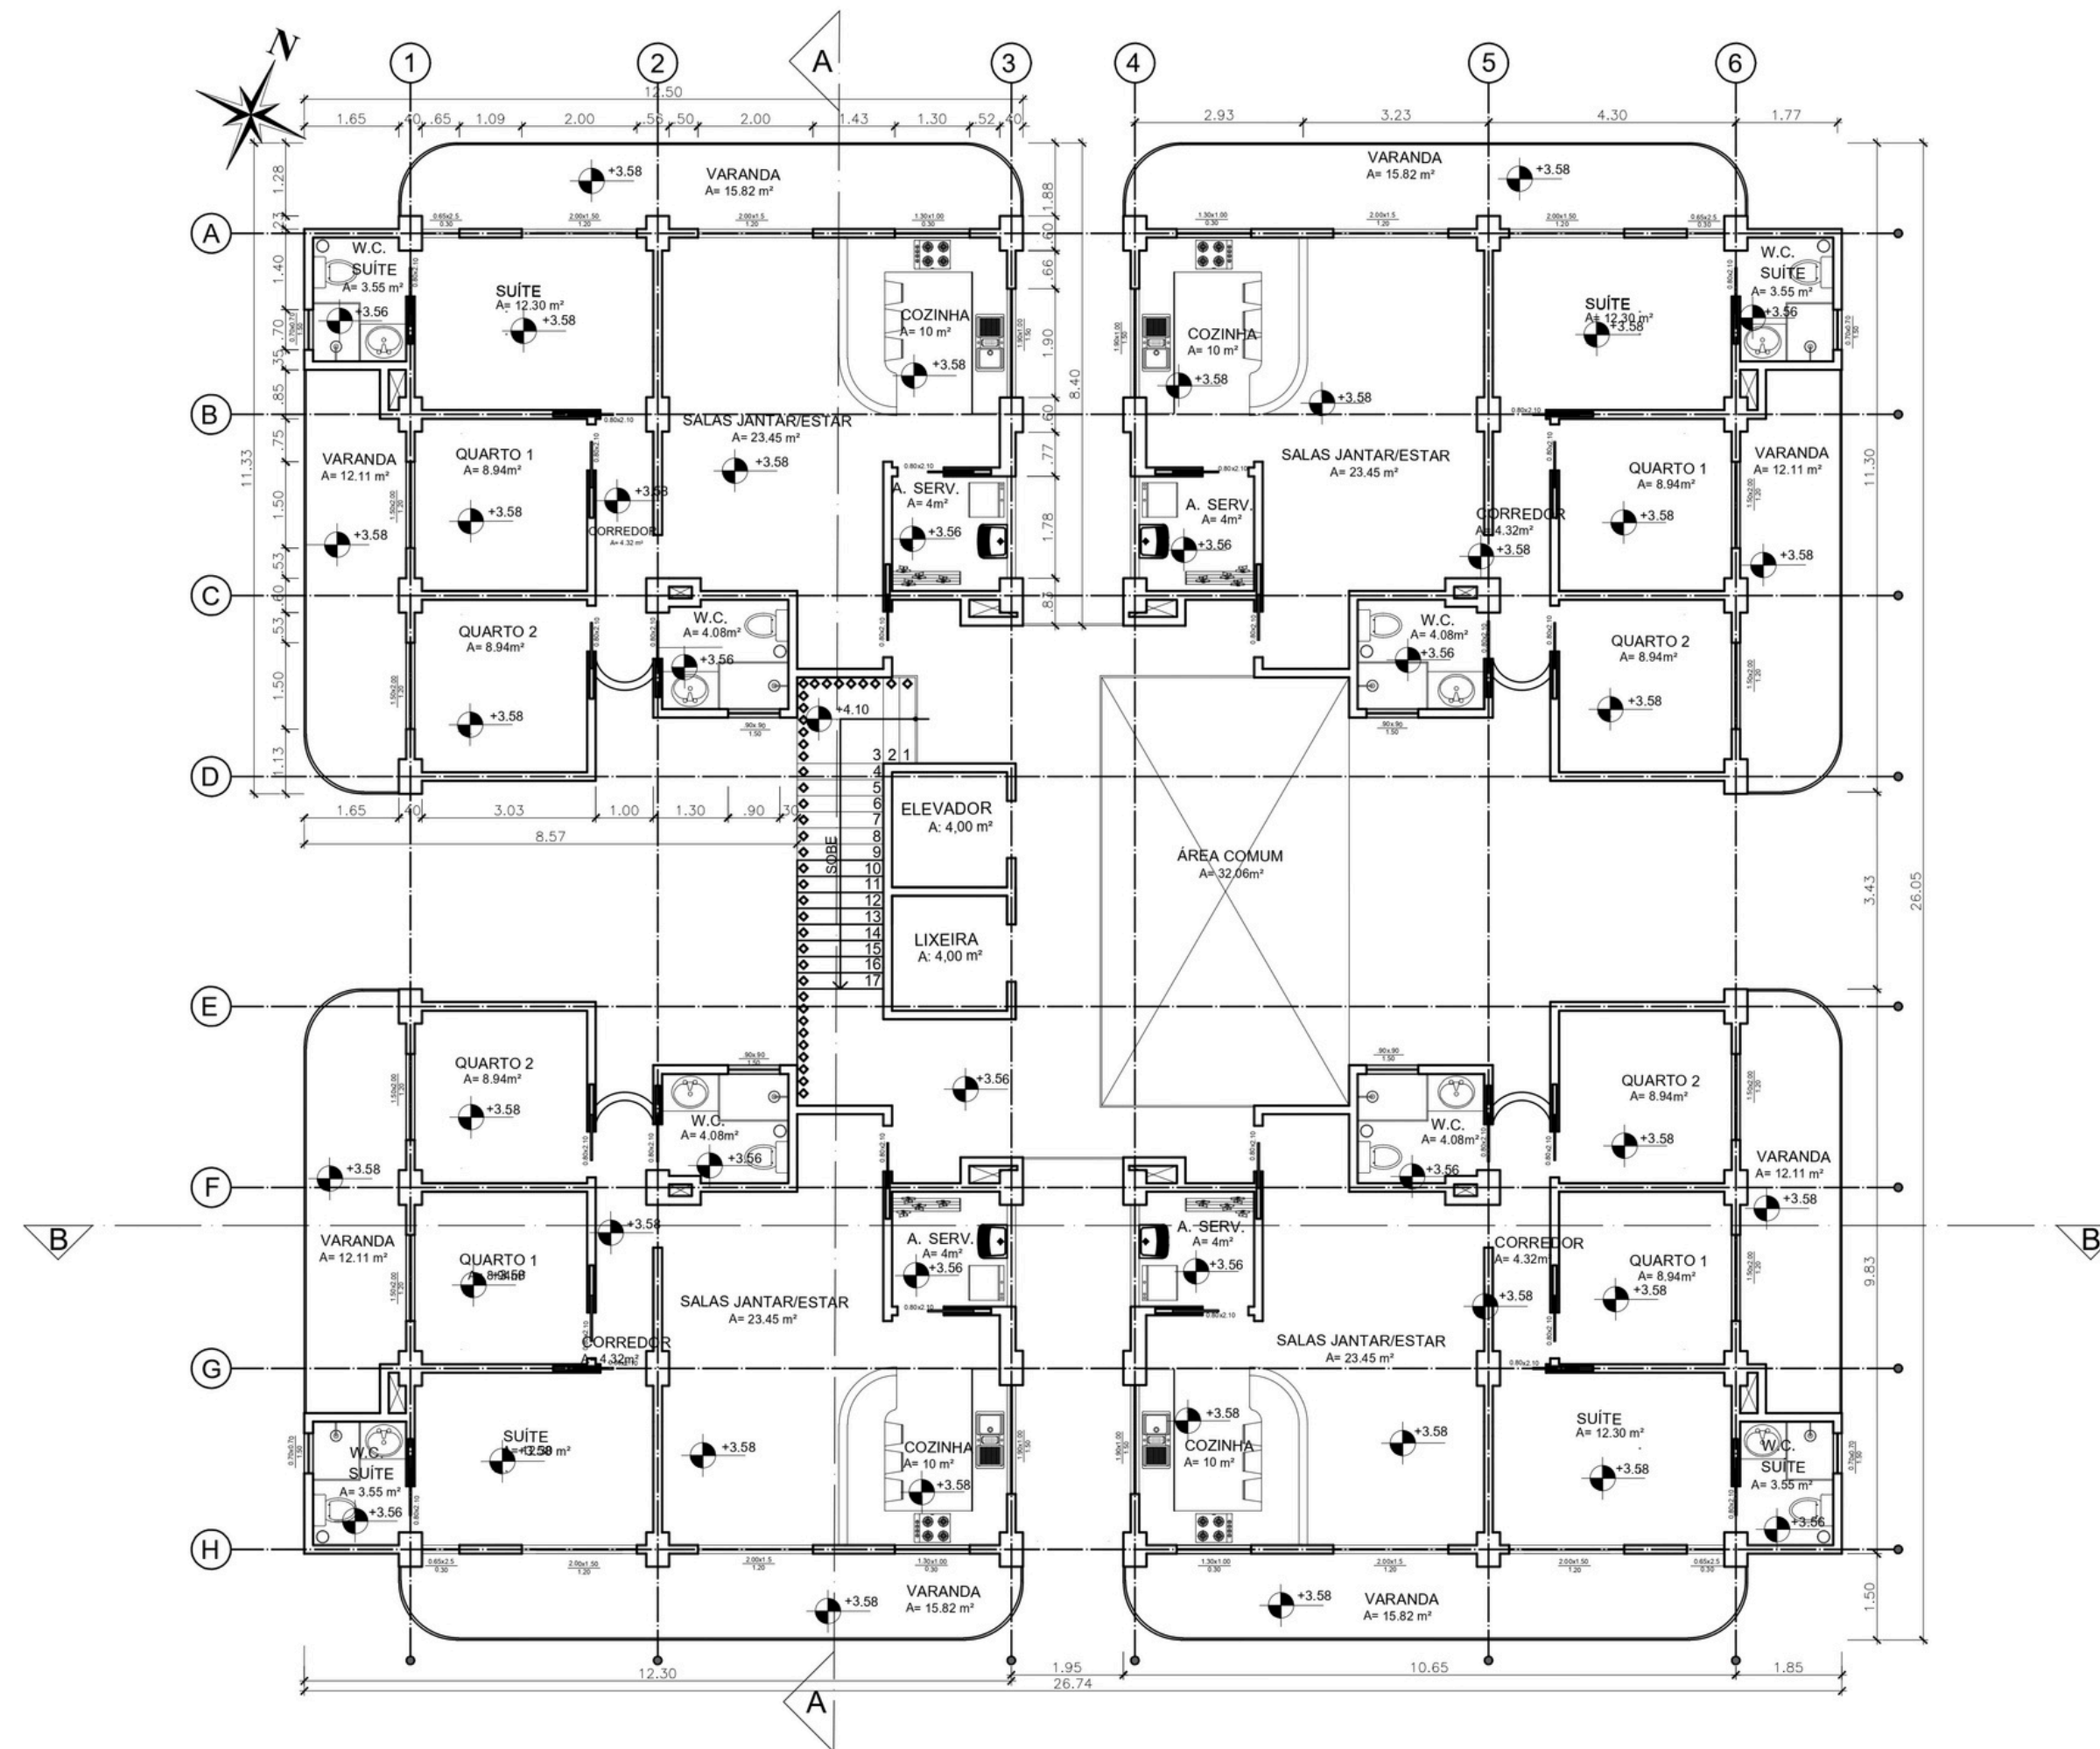

DA CONSTRUÇÃO

ÍNDICES URBANÍSTICOS

PROJETO: PROJETO DE ARQUITETURA
ESTUDO DE IMPLANTAÇÃO

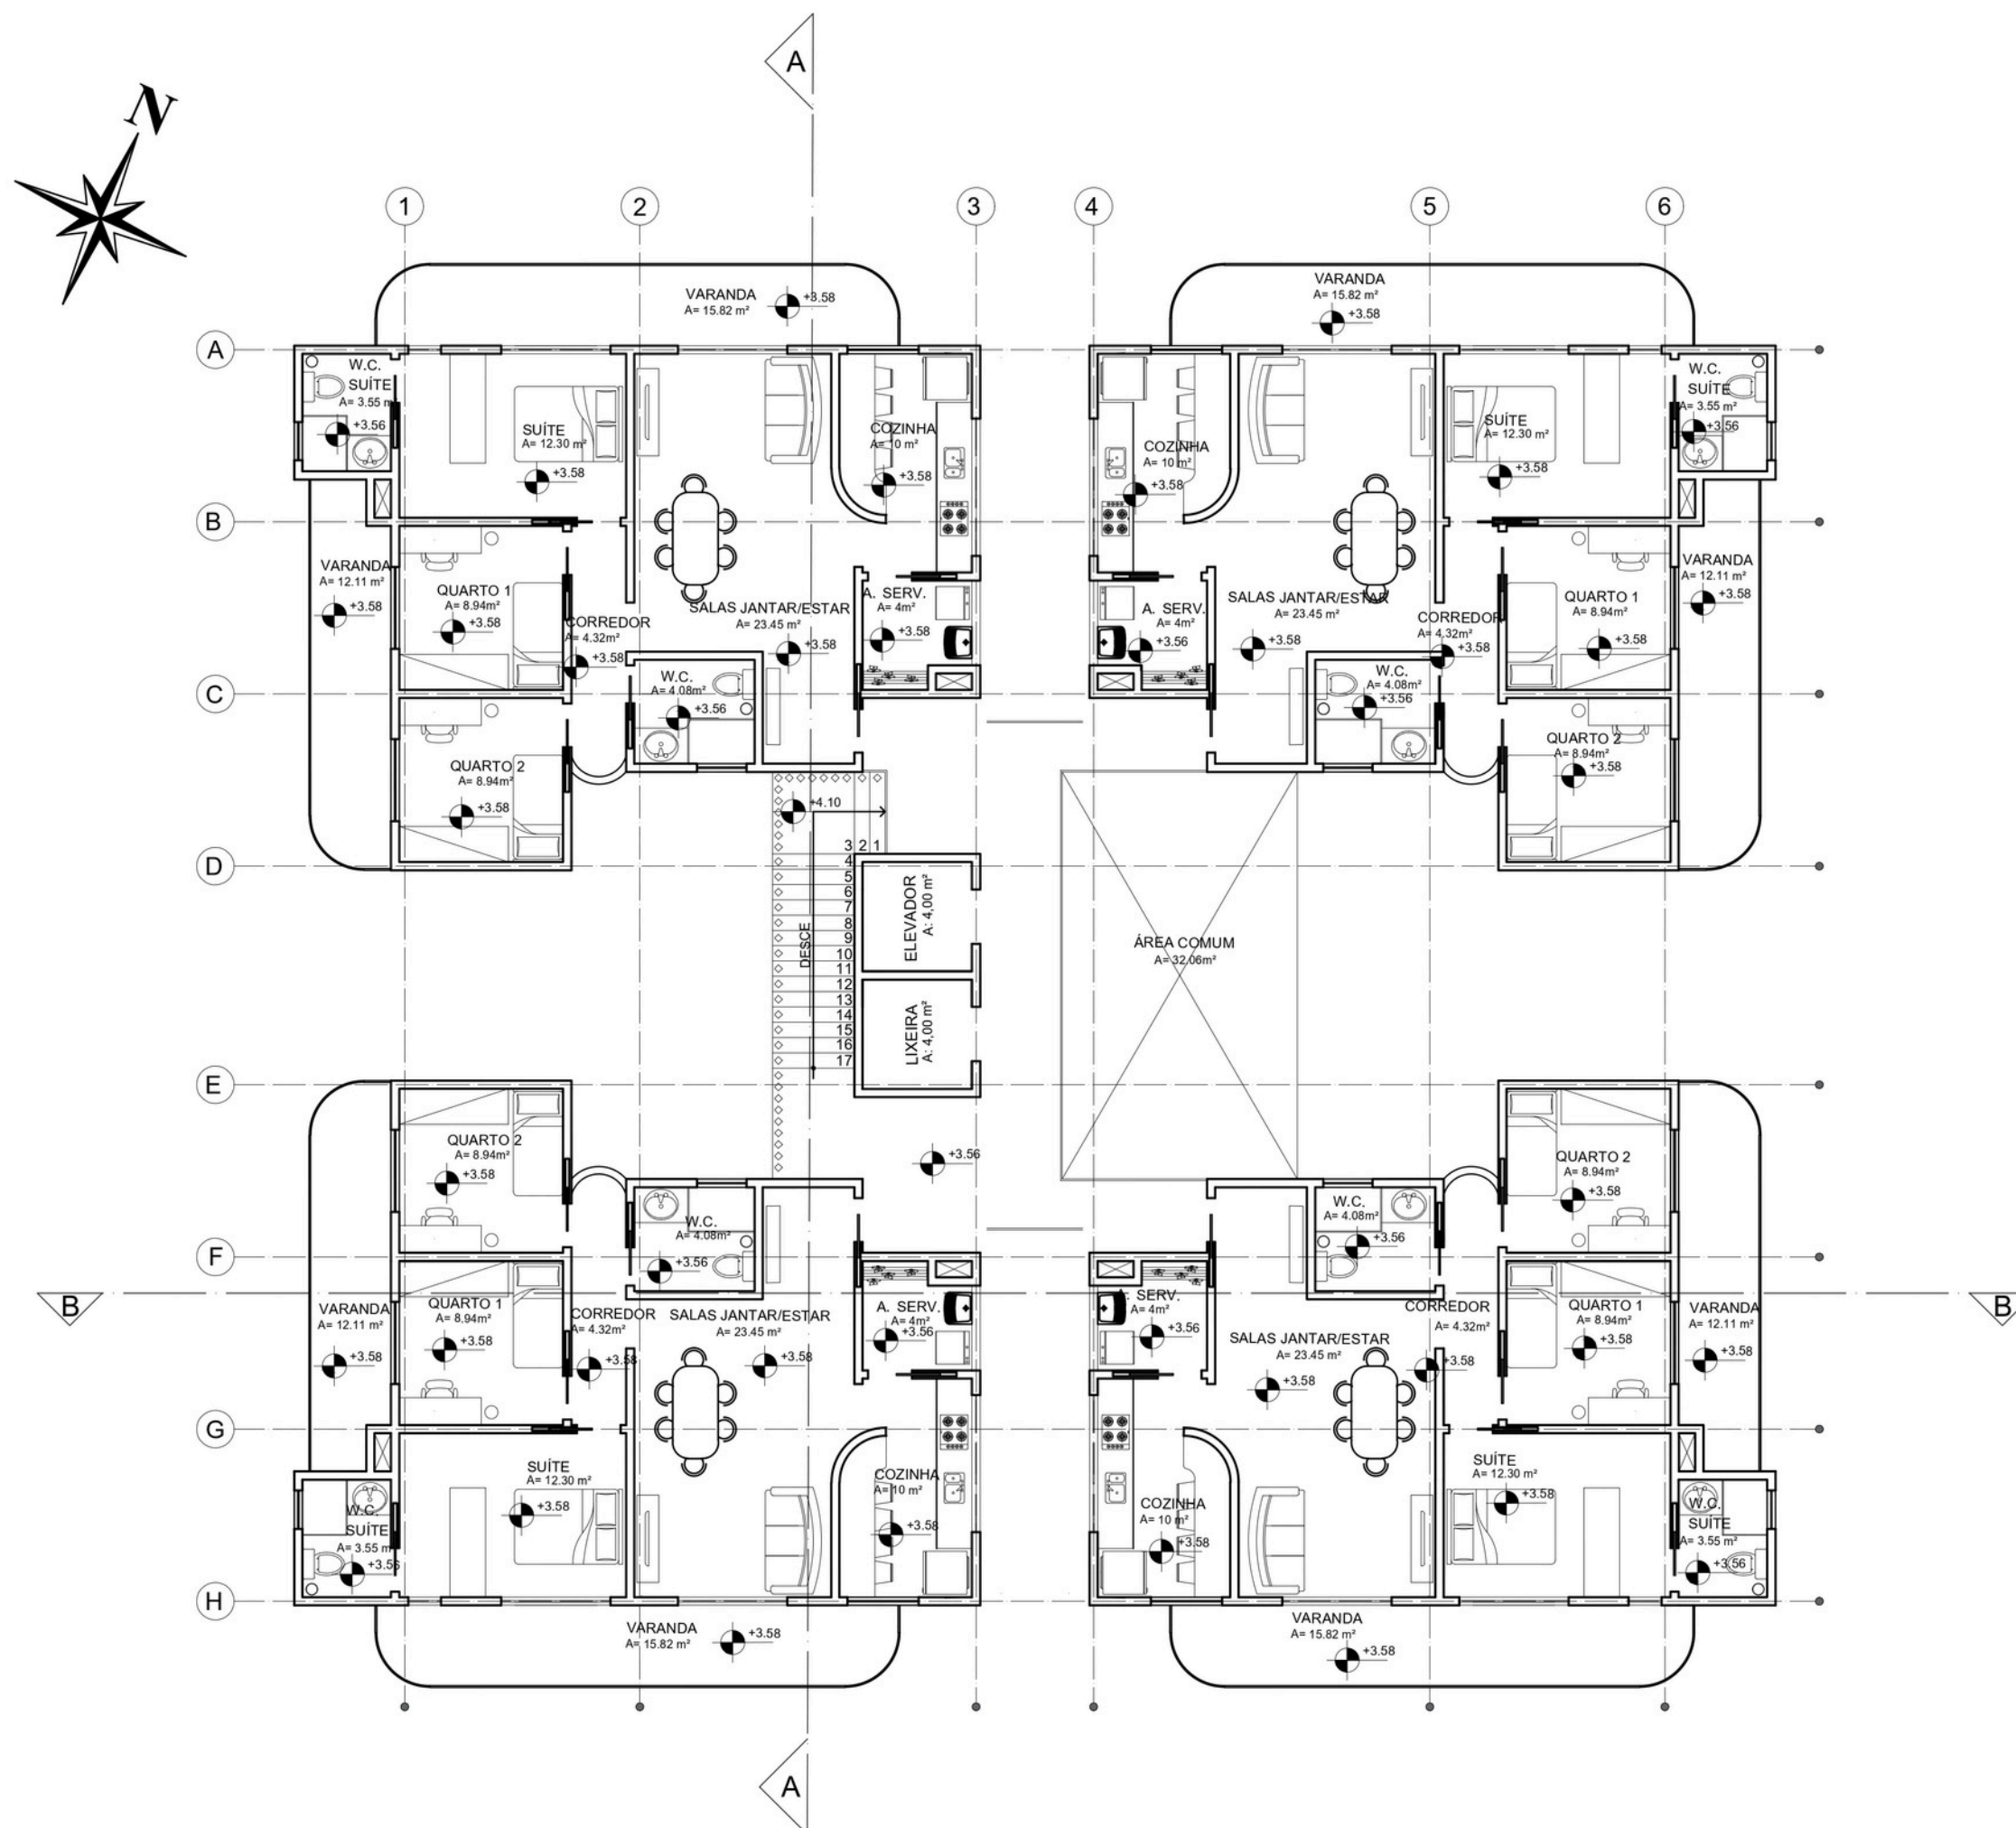

MEMORIAL DESCRITIVO

O programa de necessidades foi pensado para atender perfis variados de moradores. Além das unidades residenciais tipo, há apartamentos duplex. As áreas comuns incluem piscina com borda estilo prainha, sauna, quadra poliesportiva, salão de festas, área gourmet e jardins. Esses espaços foram posicionados visando acessibilidade, conforto e integração entre os moradores.

4

PAVIMENTO TIPO COM MOBILIÁRIO

ESCALA 1/125

ÍNDICES DA CONSTRUÇÃO

Taxa de Ocupação: 22%
Área Construída: 1.113,91m²
Área do Terreno: 4.913,79m²
Área por Edificação: 466,09m²
Área do Apartamento: 91,82m²

ÍNDICES URBANÍSTICOS

Área: 4.913,79m²
Coeficiente de aproveitamento: 4 - Decreto 13.074
Potencial construtivo: 19.655,16m²
Taxa de ocupação: 70% - Decreto 1412 - 1977
Afastamento Frontal: 3,00m
Afastamento Lateral: 1,50m Zona: ZH1

PROJETO: PROJETO DE ARQUITETURA III
ESTUDO DE IMPLANTAÇÃO

ALUNAS: IASMIN GALVÃO E LETÍCIA MARTINS

MATRÍCULAS: 2023121337 e 2023121779

PRANCHA:

ESCALA:
1/125


DESENHO:
04/12

DATA:
03/06/2025

04/12

MEMORIAL DESCRITIVO

O sistema estrutural segue um padrão de eixos definidos, o que facilita a modulação dos espaços e racionaliza a construção. Os shafts foram posicionados junto aos pilares, o que permite instalações hidráulicas e sanitárias mais organizadas, com facilidade de manutenção e menor interferência nos ambientes.

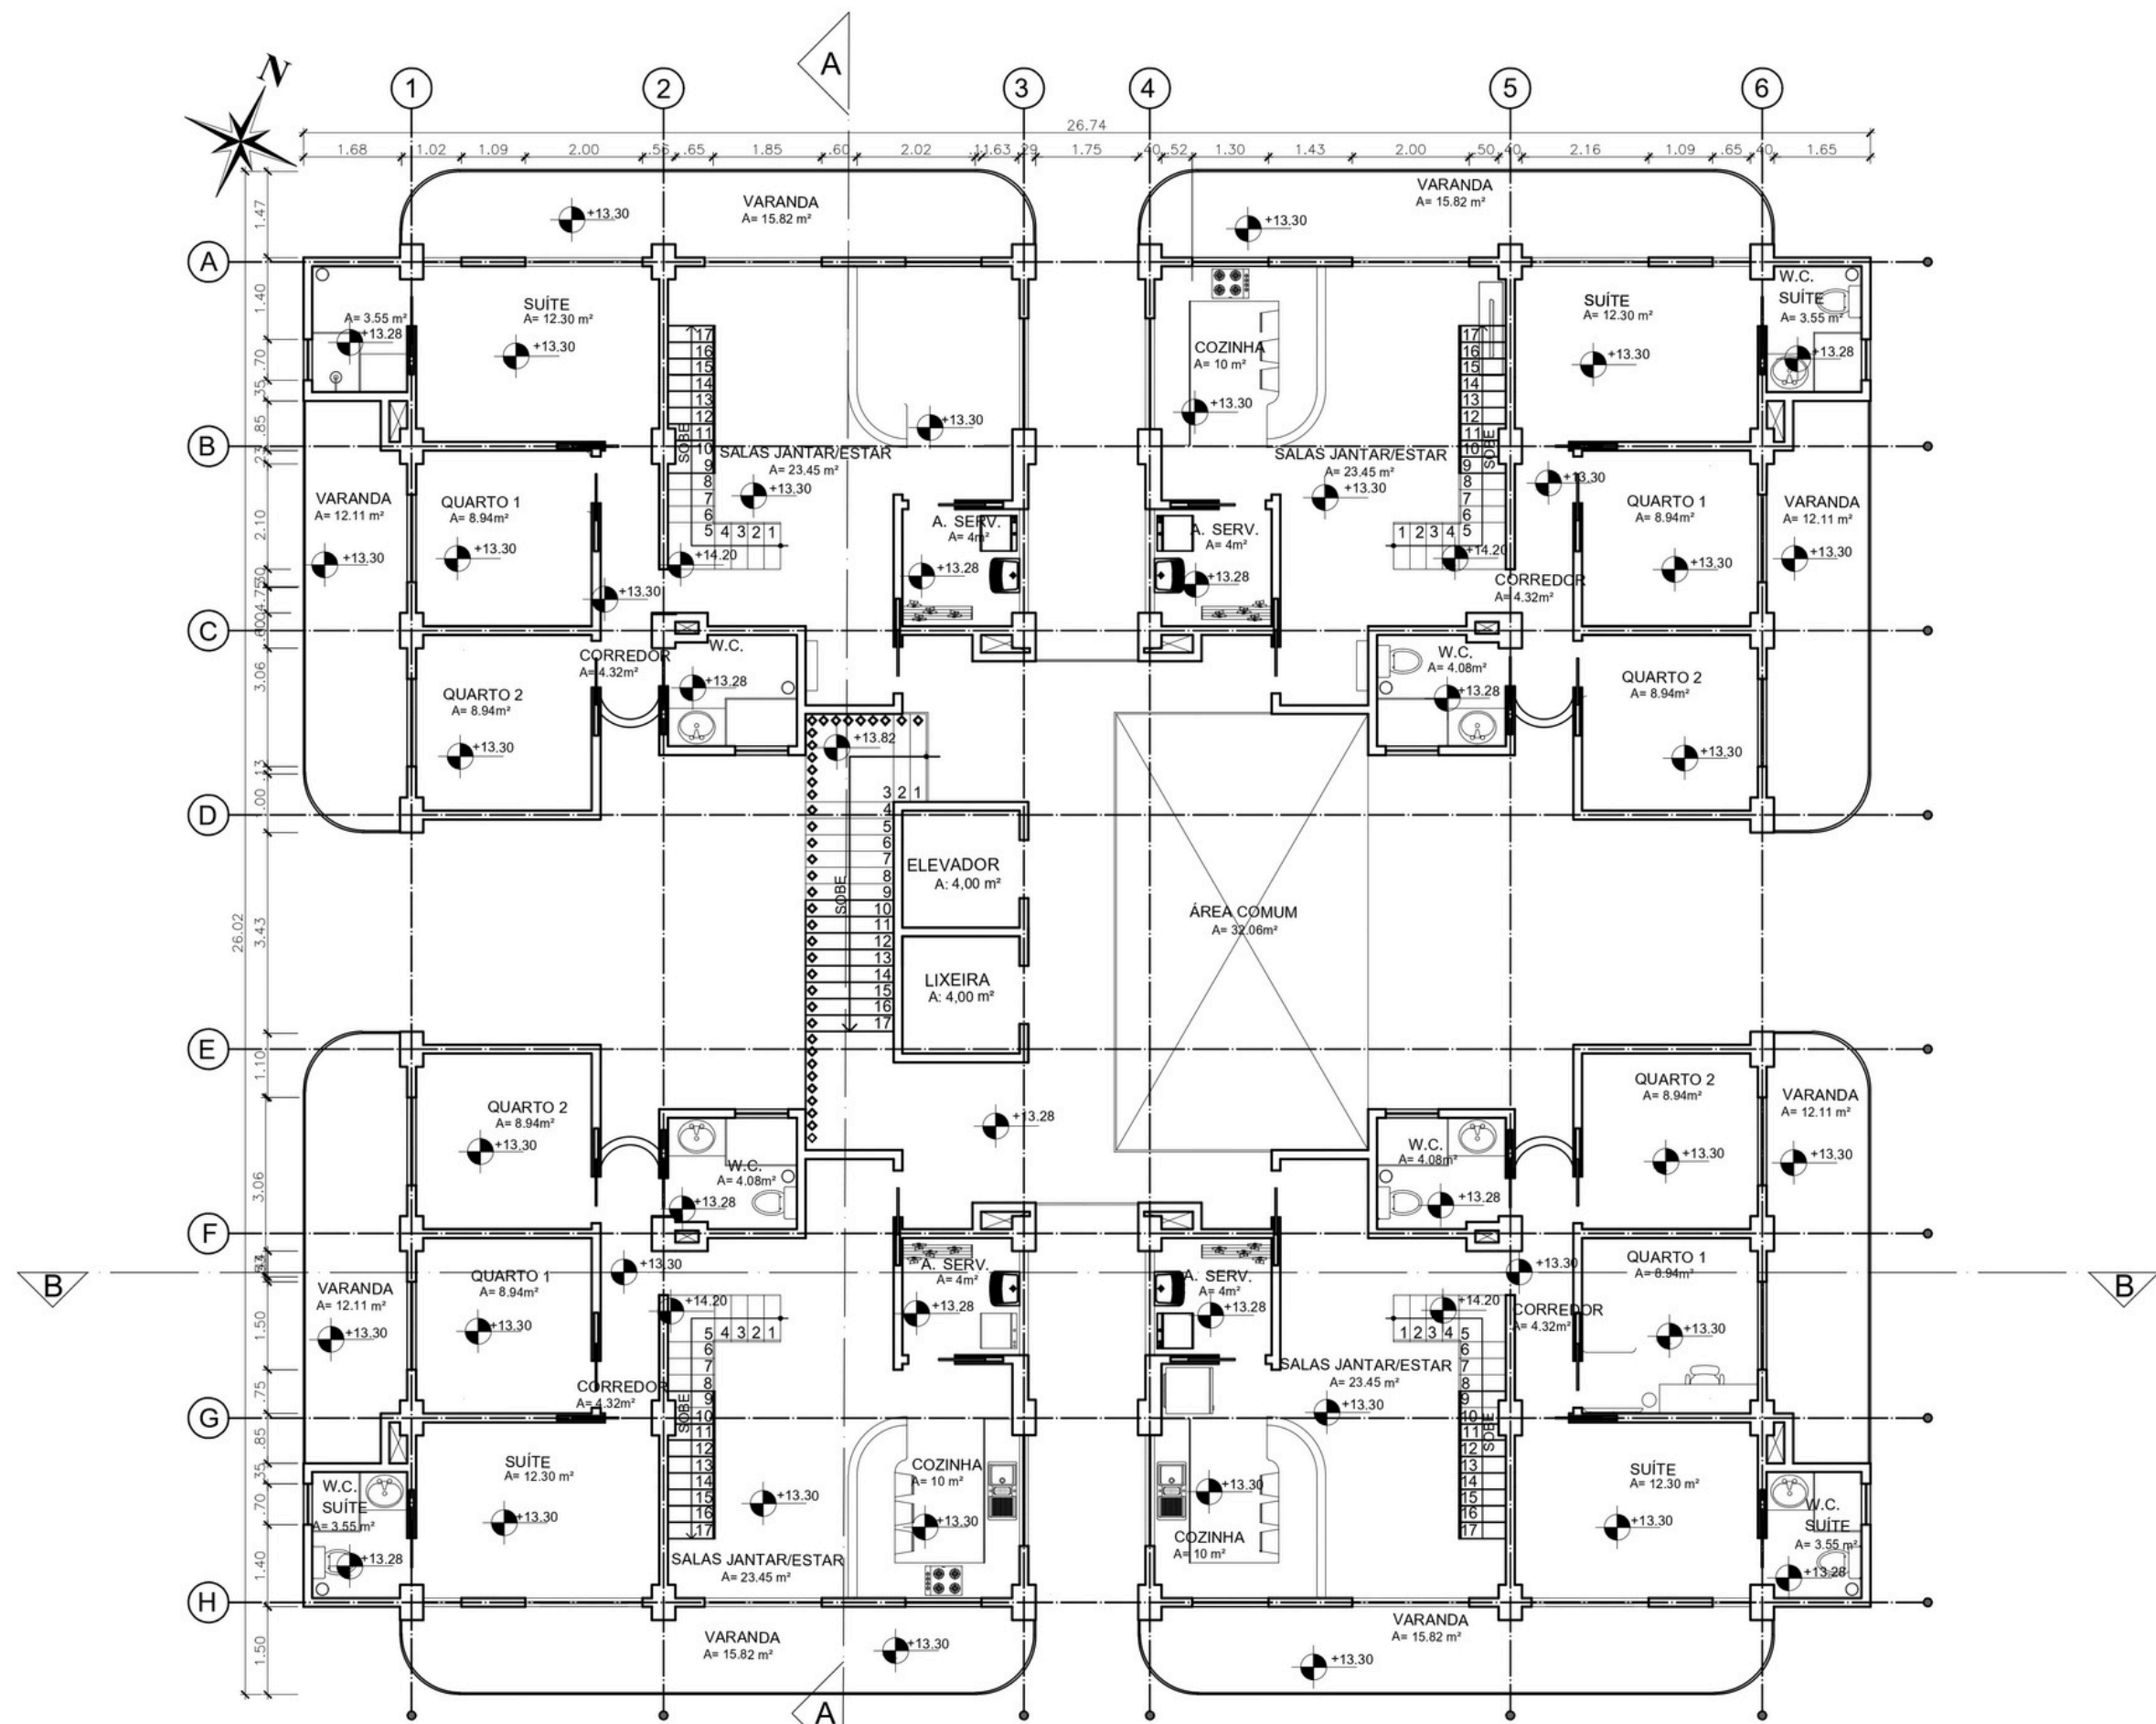

5

1º PAVIMENTO DUPLEX TÉCNICO

ESCALA 1/125

ÍNDICES DA CONSTRUÇÃO

T Taxa de Ocupação: 22%
Área Construída: 1.113,91m²
Área do Terreno: 4.913,79m²
Área por Edificação: 466,09m²
Área do Apartamento: 91,82m²

ÍNDICES URBANÍSTICOS

Área: 4.913,79m²
Coeficiente de aproveitamento: 4 - Decreto 13.074
Potencial construtivo: 19.655,16m²
Taxa de ocupação: 70% - Decreto 1412 -1977
Afastamento Frontal: 3,00m
Afastamento Lateral: 1,50m Zona: ZH1

PROJETO: PROJETO DE ARQUITETURA III
ESTUDO DE IMPLANTAÇÃO

ALUNAS: IASMIN GALVÃO E LETÍCIA MARTINS

MATRÍCULAS: 2023121337 e 2023121779


PRANCHA:

ESCALA:
1/125

DESENHO:
05/12

DATA:
03/06/2025

05/12

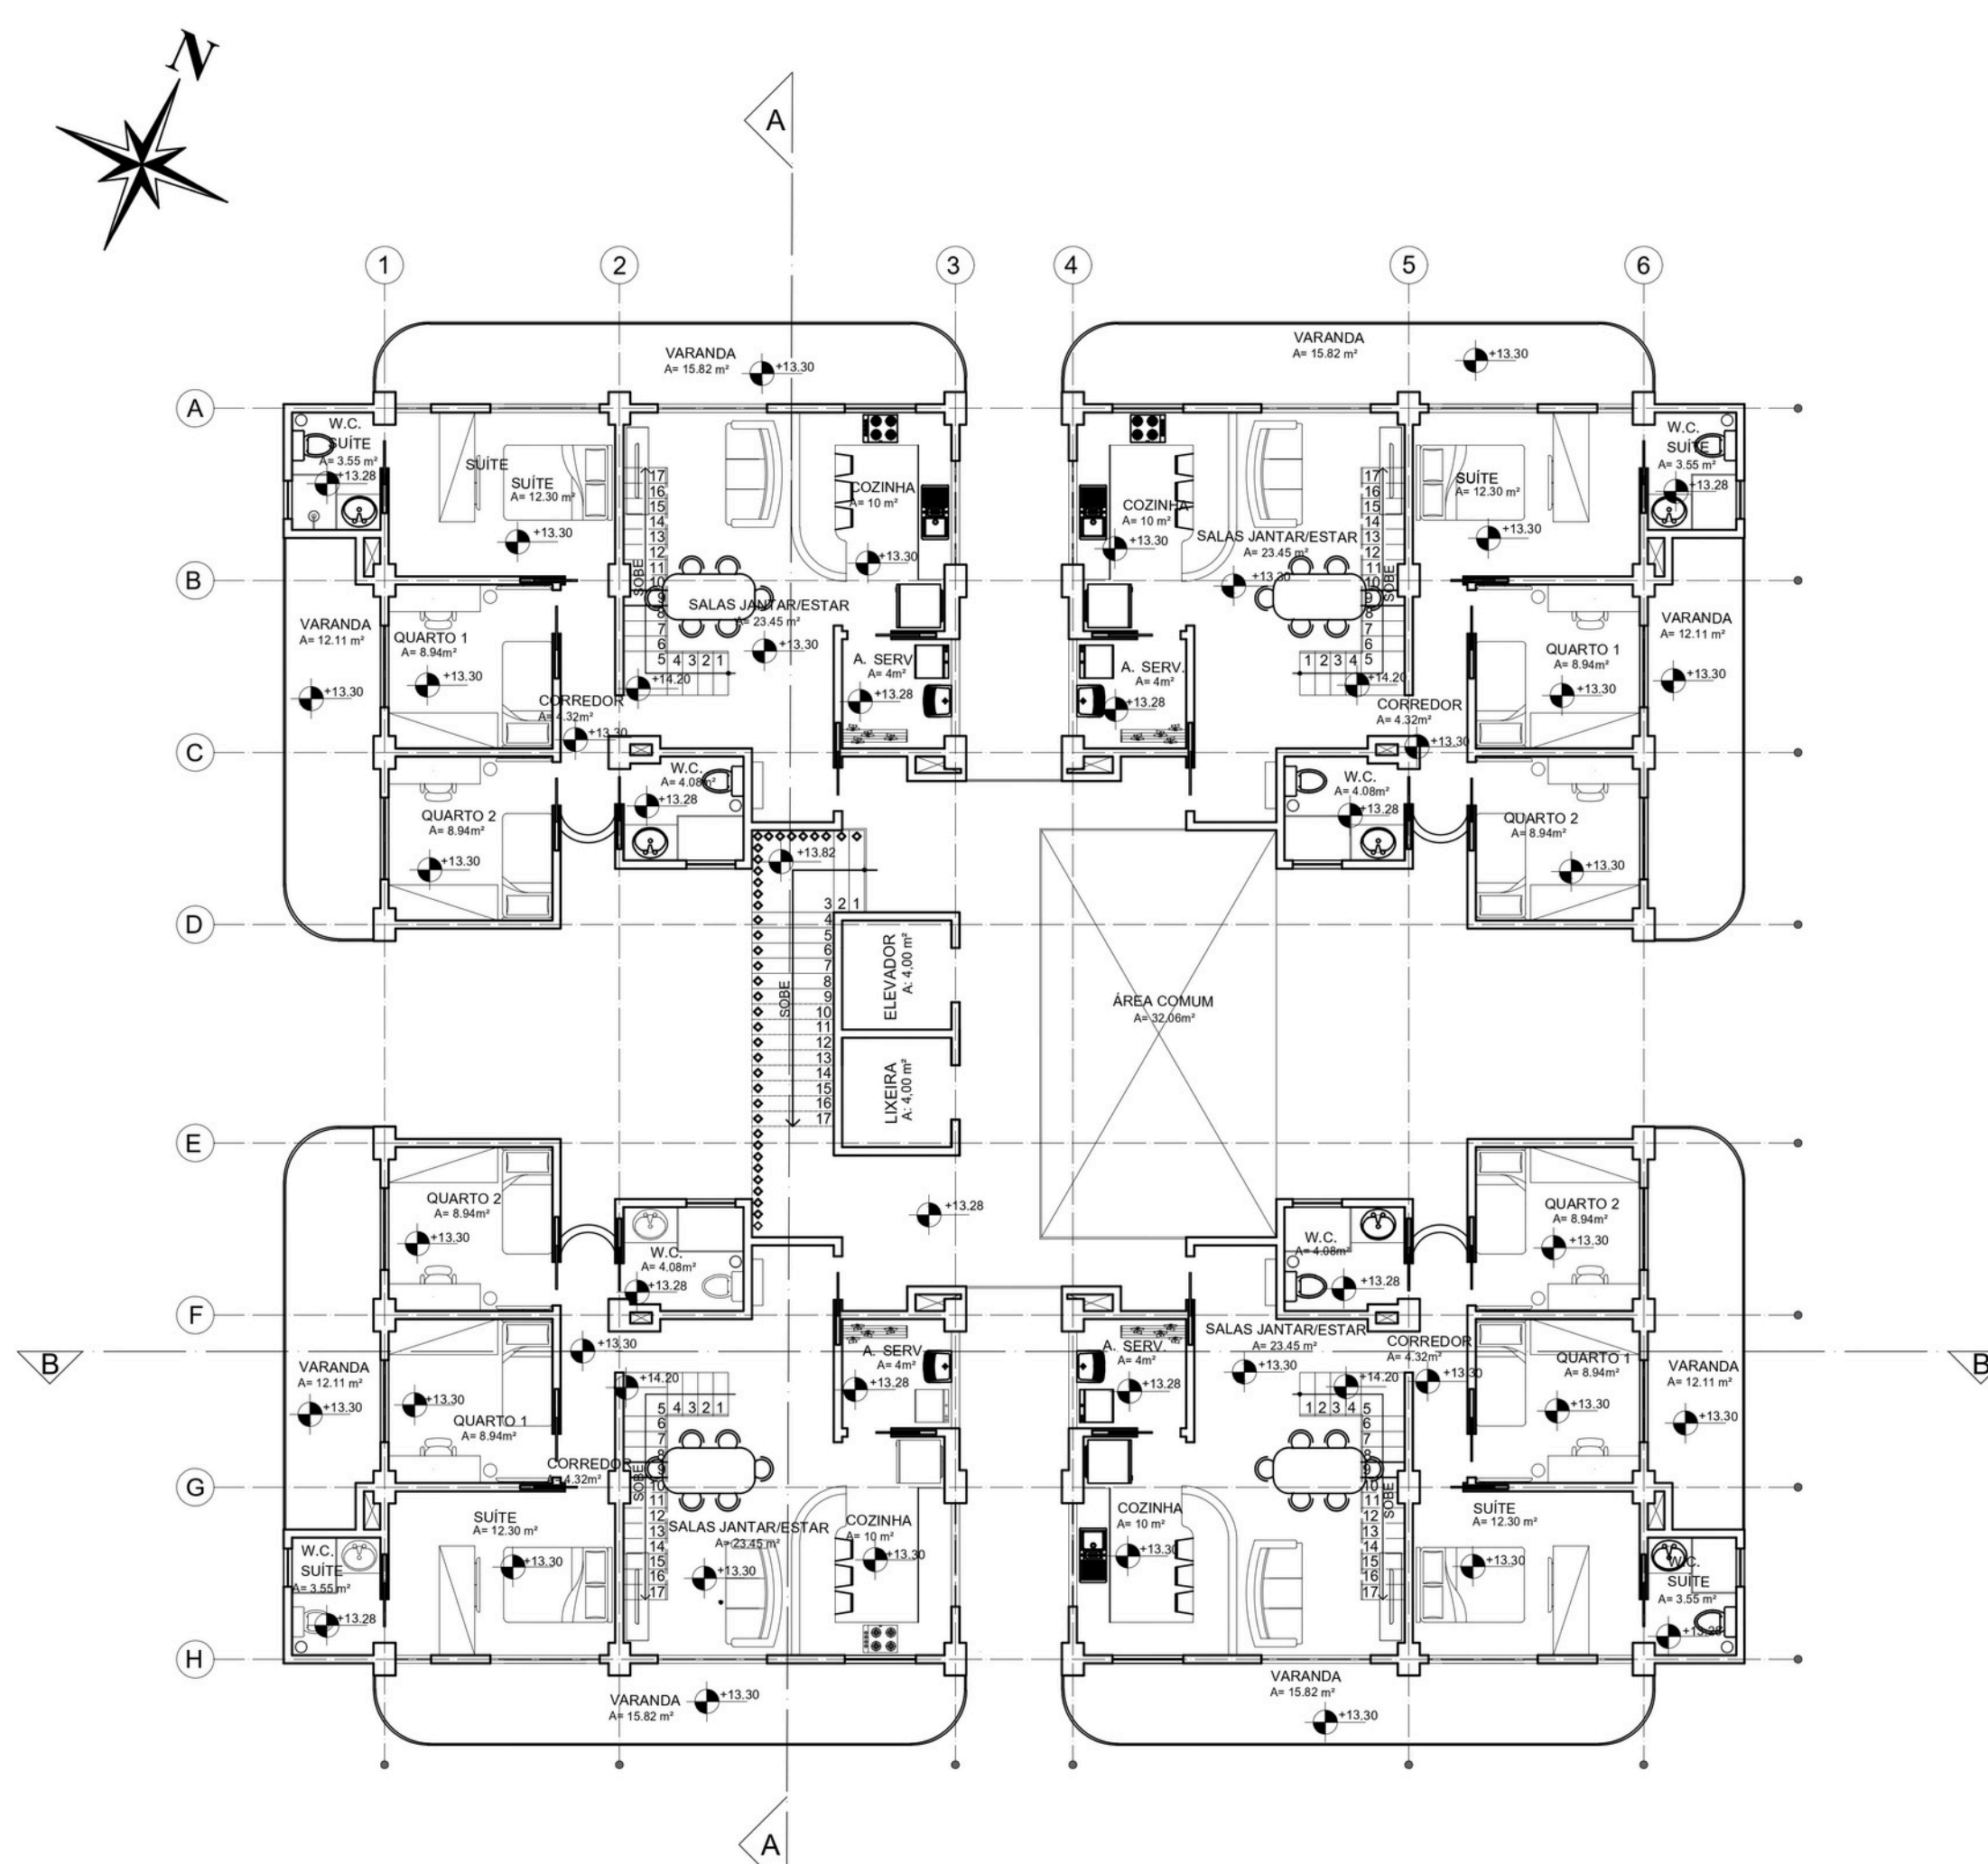

MEMORIAL DESCRITIVO

A volumetria dos edifícios foi resolvida com formas simples e proporcionais, respeitando o entorno e criando fachadas bem resolvidas com o uso de elementos como janelas amplas, cobogós e varandas. Esses recursos, inspirados na arquitetura brasileira, garantem entrada de luz e ar nos ambientes internos, além de dar identidade visual ao projeto.

ÍNDICES DA CONSTRUÇÃO

Taxa de Ocupação: 22%
Área Construída: 1.113,91m²
Área do Terreno: 4.913,79m²
Área por Edificação: 466,09m²
Área do Apartamento: 91,82m²

ÍNDICES URBANÍSTICOS


Área: 4.913,79m²
Coeficiente de aproveitamento: 4 - Decreto 13.074
Potencial construtivo: 19.655,16m²
Taxa de ocupação: 70% - Decreto 1412 -1977
Afastamento Frontal: 3,00m
Afastamento Lateral: 1,50m Zona: ZH1

PROJETO: PROJETO DE ARQUITETURA III			PRANCHA: 06/12
ESTUDO DE IMPLANTAÇÃO			
ALUNAS: IASMIN GALVÃO E LETÍCIA MARTINS			
MATRÍCULAS: 2023121337 e 2023121779			
ESCALA: 1/125	DESENHO: 06/12	DATA: 03/06/2025	

MEMORIAL DESCRITIVO

A circulação vertical foi planejada com atenção. As escadas foram posicionadas junto ao núcleo de elevadores e lixeiras e contam com aberturas para entrada de luz e ventilação natural. A estrutura metálica leve, com elementos vazados, também compõe visualmente as fachadas.

As coberturas foram projetadas de forma que fosse possível aproveitar o máximo de espaço livre, trazendo conforto aos moradores.

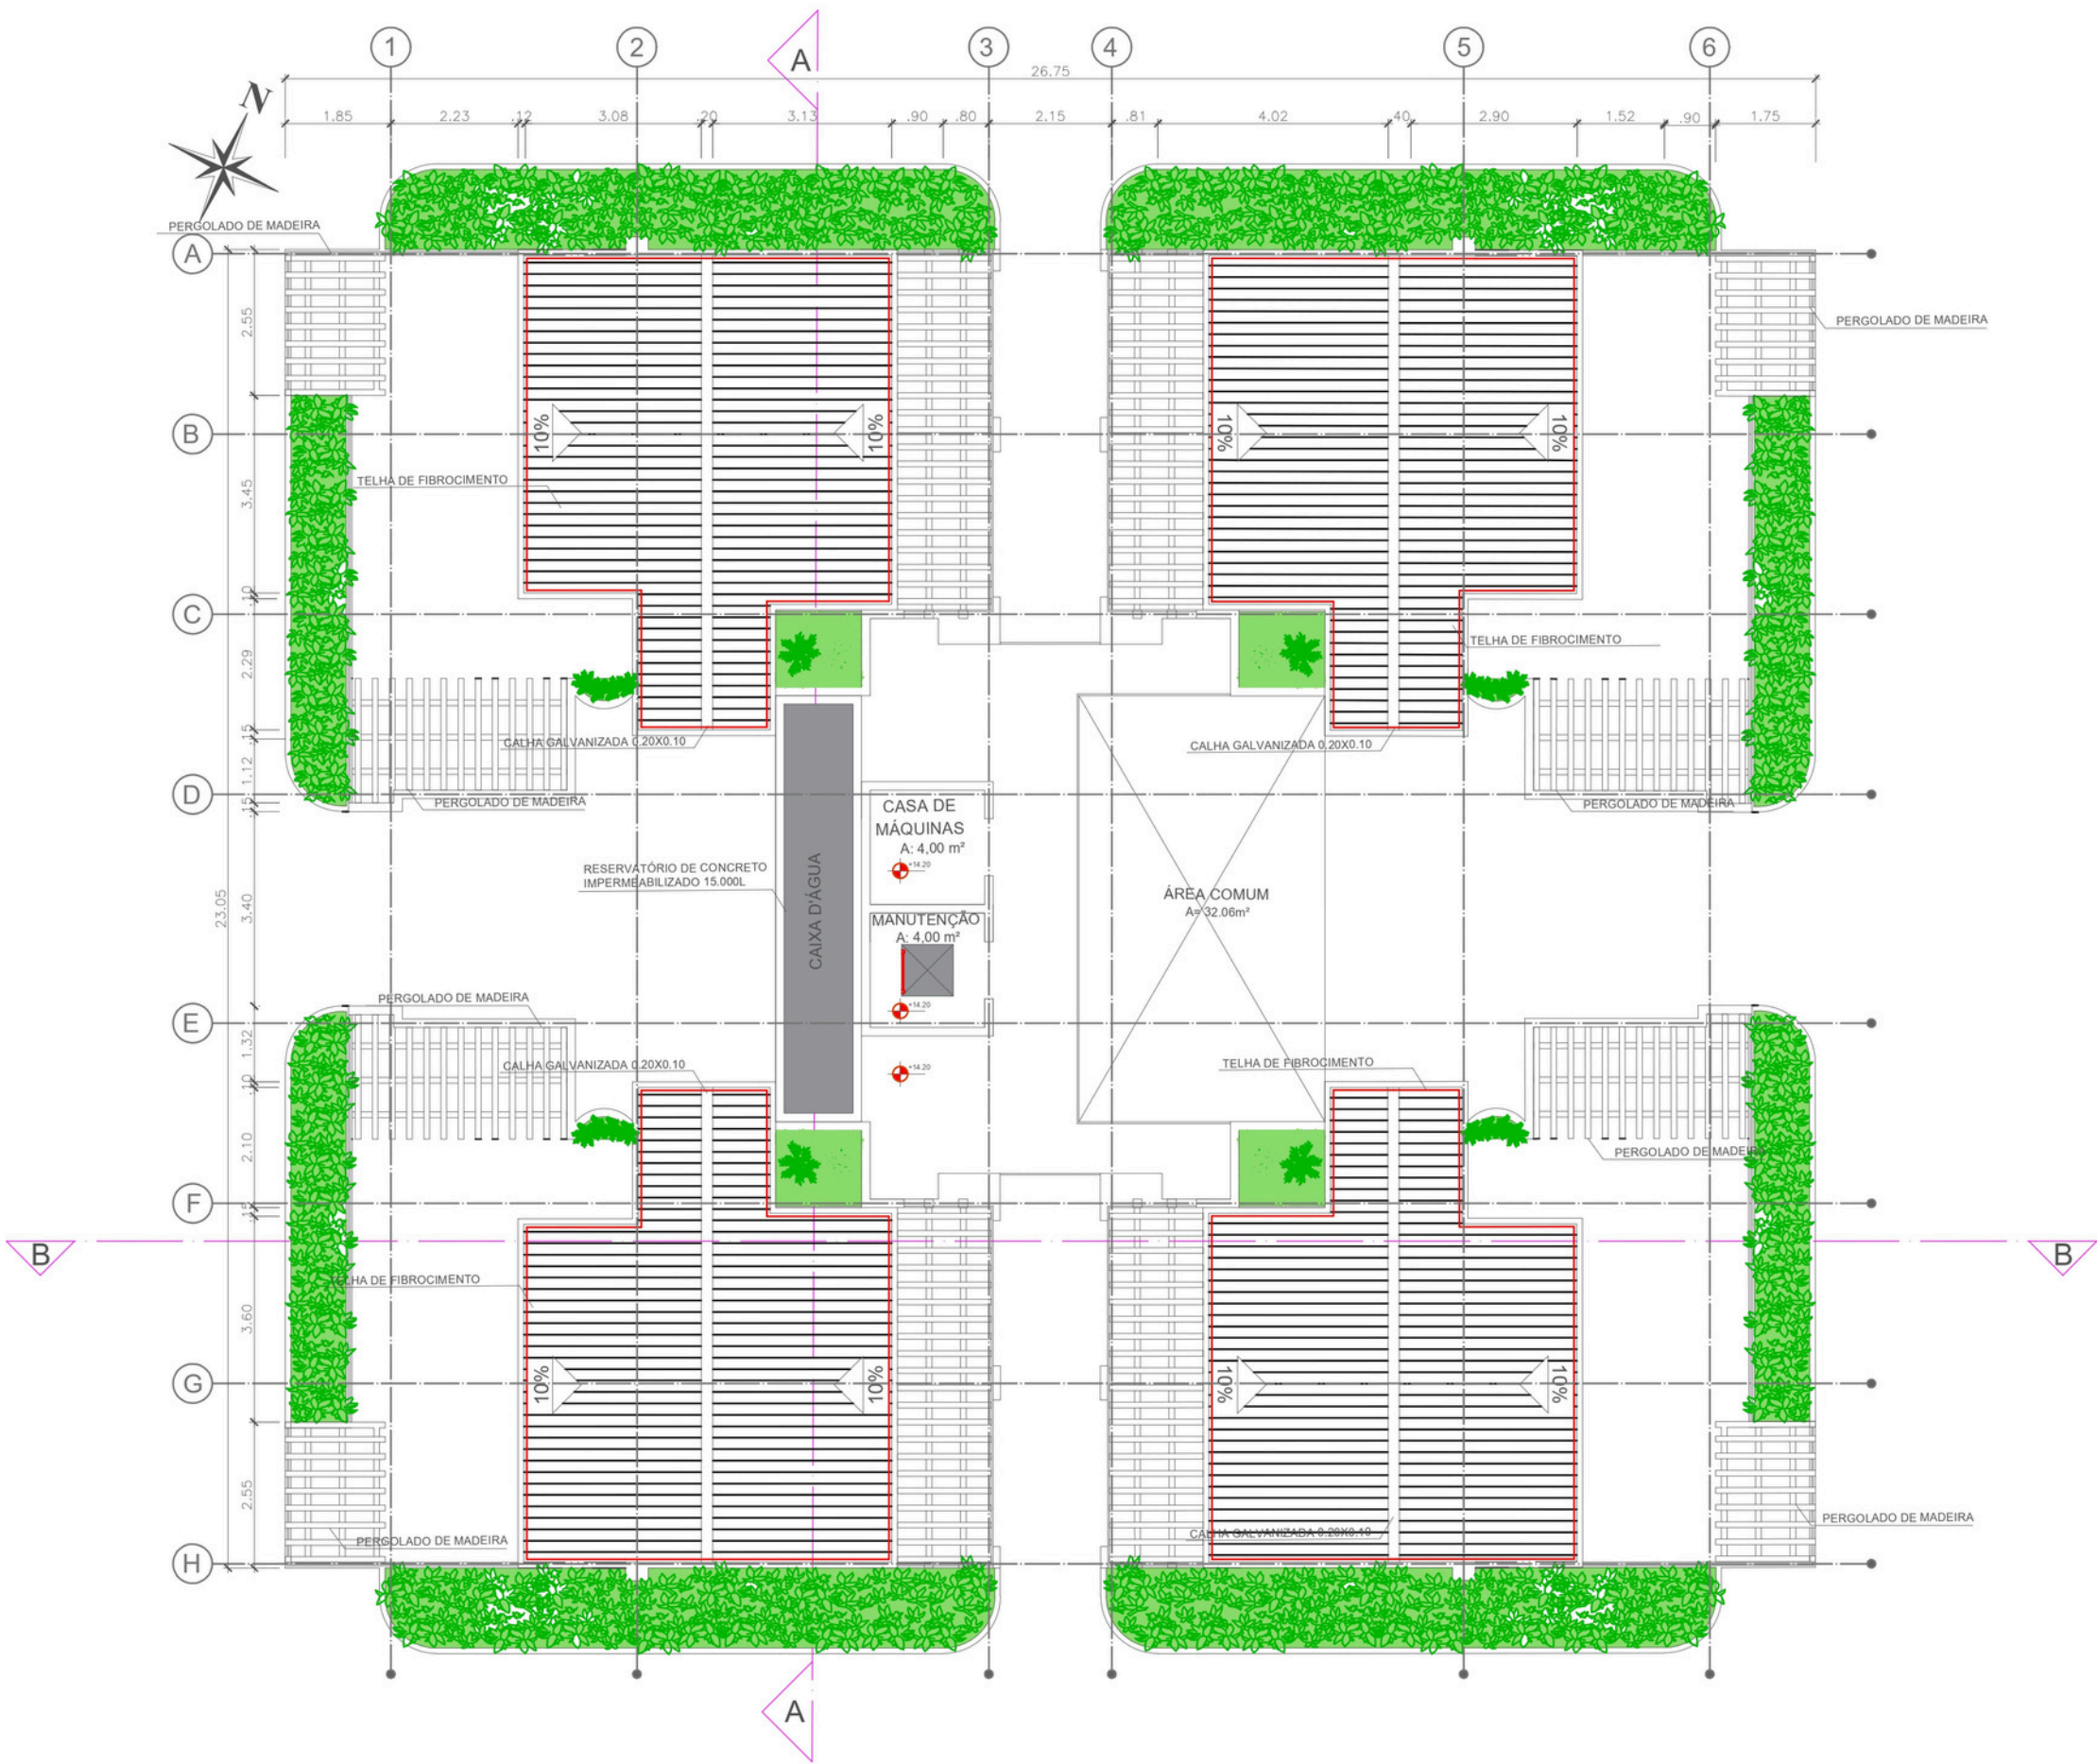

7

2º PAVIMENTO DUPLEX - TÉCNICO

ESCALA 1/125

ÍNDICES DA CONSTRUÇÃO

Taxa de Ocupação: 22%
Área Construída: 1.113,91m²
Área do Terreno: 4.913,79m²
Área por Edificação: 466,09m²
Área do Apartamento: 91,82m²

ÍNDICES URBANÍSTICOS

Área: 4.913,79m²
Coeficiente de aproveitamento: 4 - Decreto 13.074
Potencial construtivo: 19.655,16m²
Taxa de ocupação: 70% - Decreto 1412 -1977
Afastamento Frontal: 3,00m
Afastamento Lateral: 1,50m Zona: ZH1

PROJETO: PROJETO DE ARQUITETURA III
ESTUDO DE IMPLANTAÇÃO

ALUNAS: IASMIN GALVÃO E LETÍCIA MARTINS

MATRÍCULAS: 2023121337 e 2023121779


PRANCHA:

ESCALA:
1/125

DESENHO:
07/12

DATA:
03/06/2025

07/12

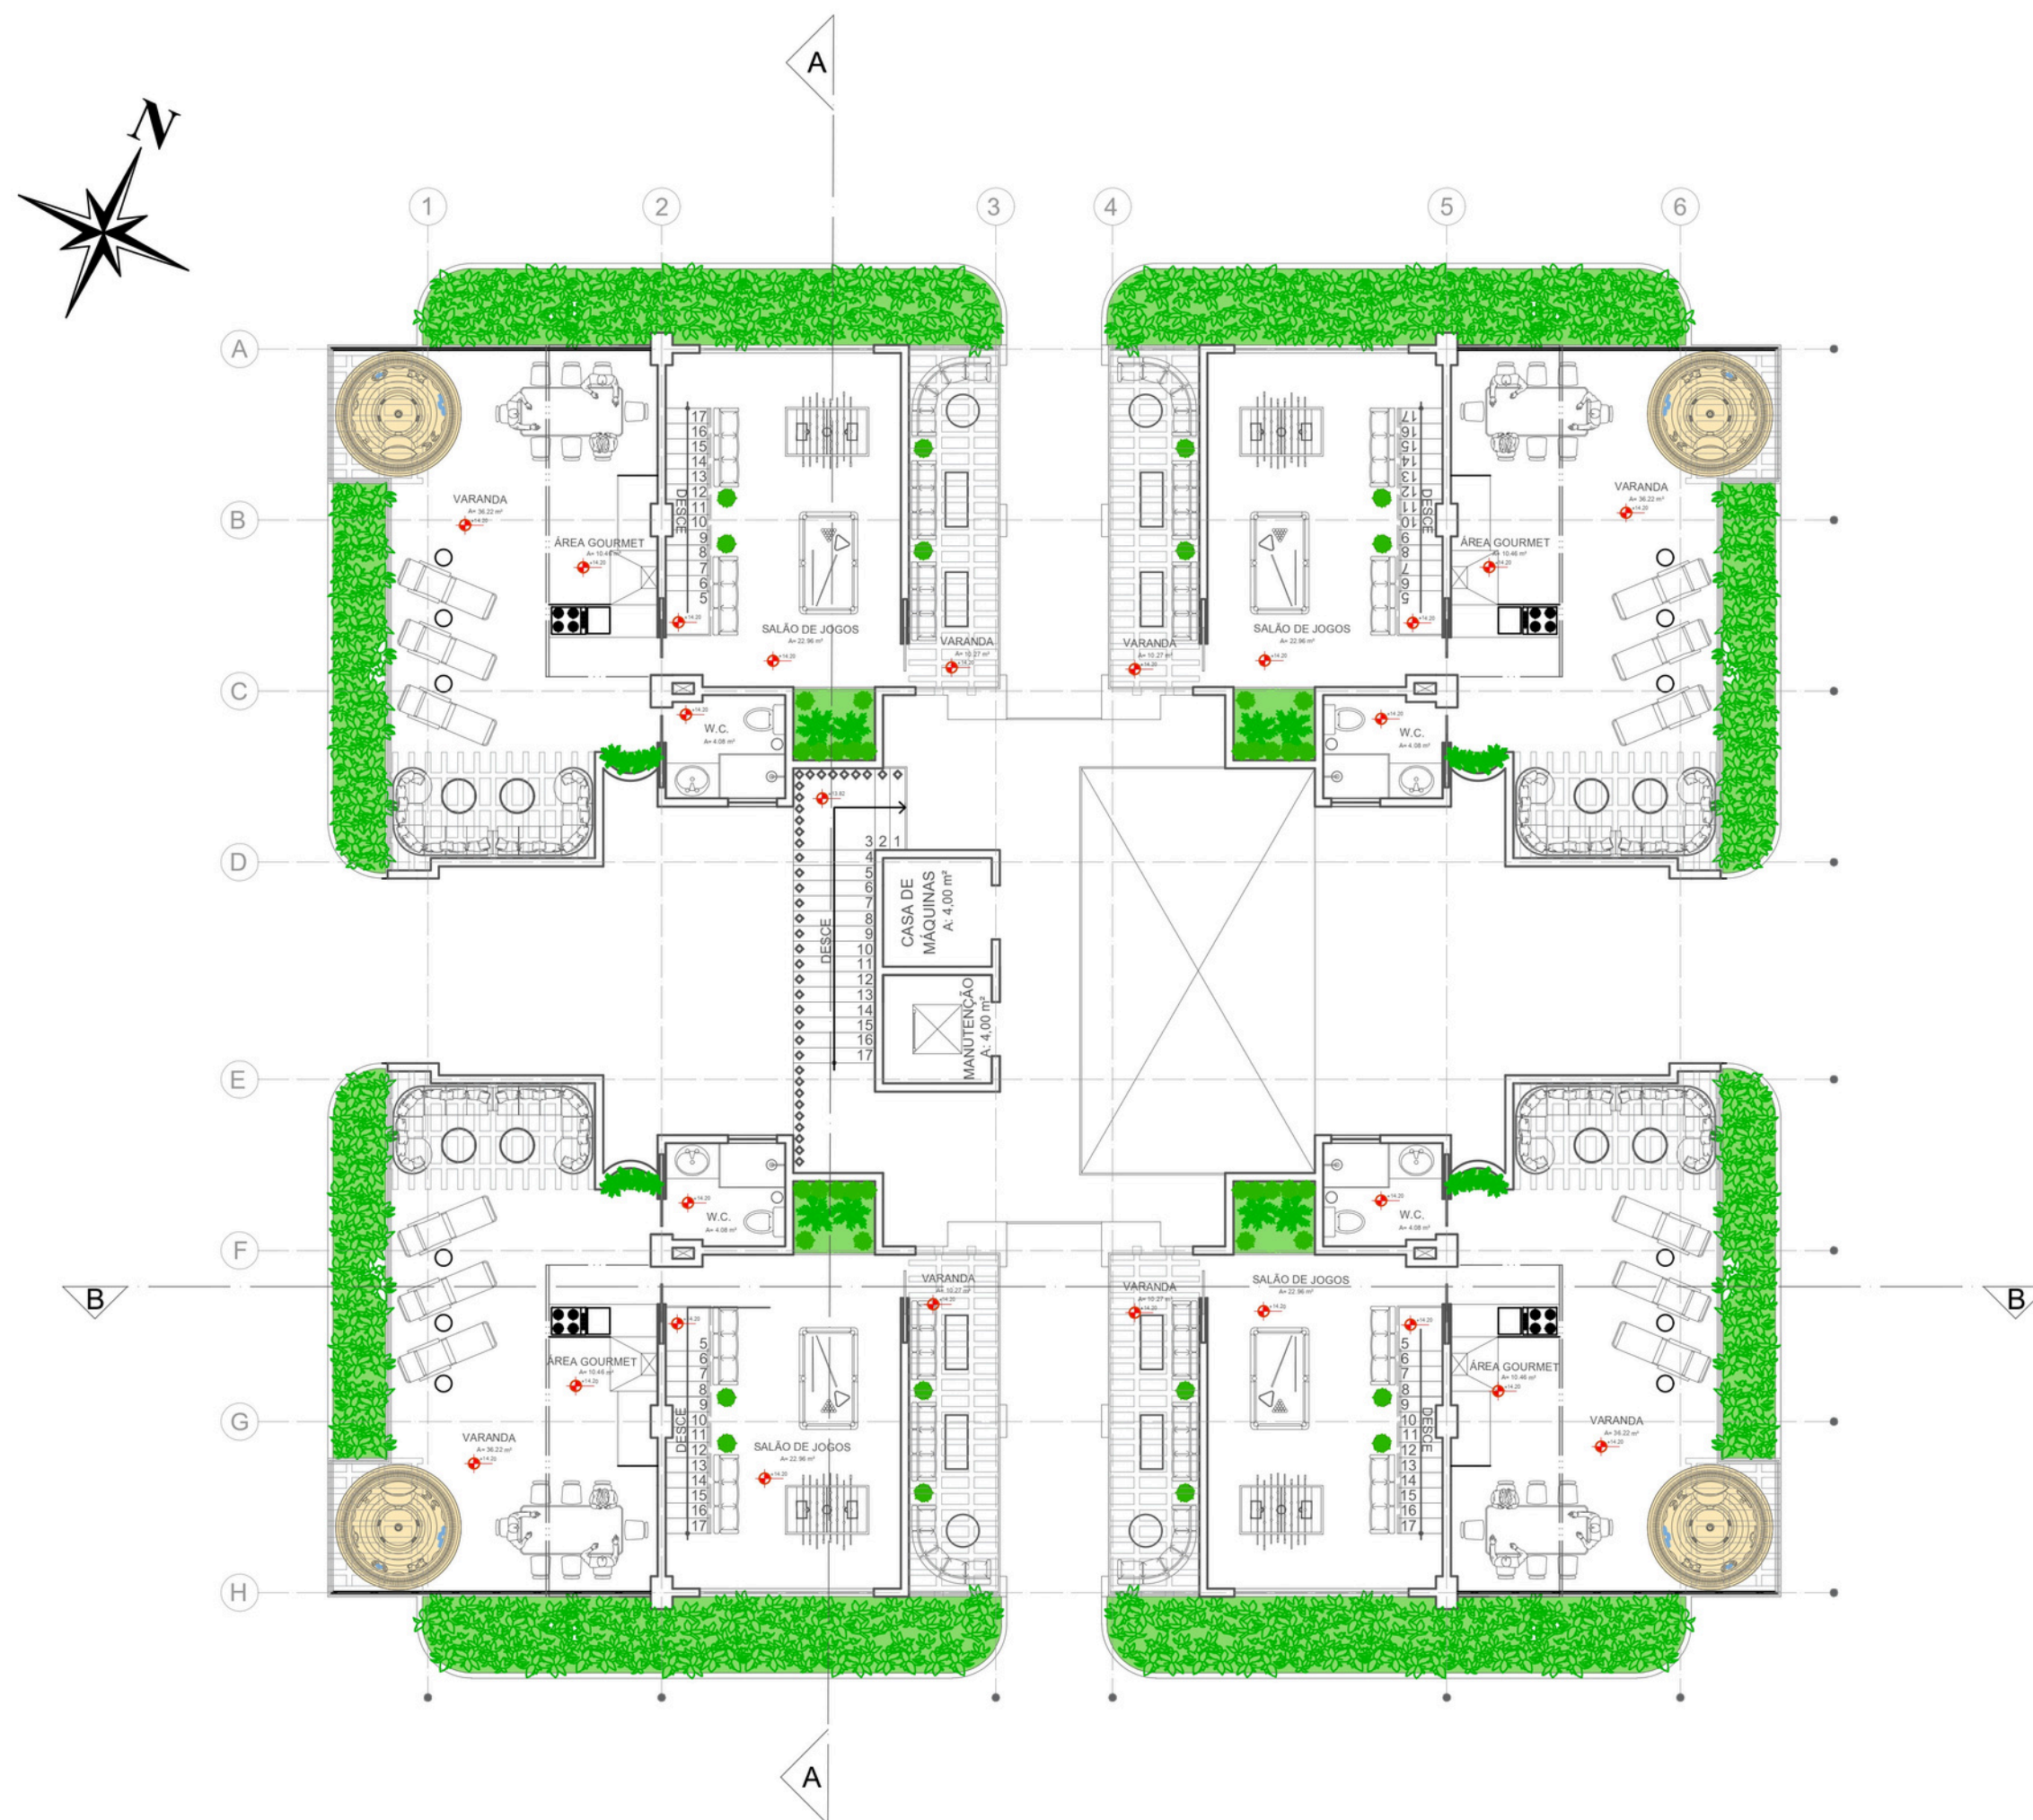

MEMORIAL DESCRITIVO

Ainda buscando maior conforto e privacidade, o duplex conta com um espaço próprio para lazer: salão de jogos, hidromassagem e área gourmet. Um ambiente amplo, com bom aproveitamento dos espaços e bastante vegetação.

8

2º PAVIMENTO DUPLEX - MOBILIÁRIO

ESCALA 1/125

ÍNDICES DA CONSTRUÇÃO

Taxa de Ocupação: 22%
Área Construída: 1.113,91m²
Área do Terreno: 4.913,79m²
Área por Edificação: 466,09m²
Área do Apartamento: 91,82m²

ÍNDICES URBANÍSTICOS

Área: 4.913,79m²
Coeficiente de aproveitamento: 4 - Decreto 13.074
Potencial construtivo: 19.655,16m²
Taxa de ocupação: 70% - Decreto 1412 -1977
Afastamento Frontal: 3,00m
Afastamento Lateral: 1,50m Zona: ZH1

PROJETO: PROJETO DE ARQUITETURA III
ESTUDO DE IMPLANTAÇÃO

ALUNAS: IASMIN GALVÃO E LETÍCIA MARTINS

MATRÍCULAS: 2023121337 e 2023121779

PRANCHA:

ESCALA:
1/125

DESENHO:
08/12


DATA:
03/06/2025

08/12

MEMORIAL DESCRITIVO

A cobertura adota platibanda com telhas de fibrocimento e inclinação de 10%, direcionando a água da chuva para uma calha central. O uso de pergolados em áreas da cobertura contribui para o cumprimento da legislação e proporciona conforto térmico nas áreas externas. No topo do edifício, foi instalada uma casa de máquinas e uma caixa d'água com capacidade de 14.633,33 litros, com acesso técnico por escada marinho e alçapão, garantindo praticidade e segurança.

No geral, o projeto busca oferecer qualidade de vida por meio de soluções arquitetônicas que respeitam o clima local, atendem à legislação, valorizam o uso do verde e promovem conforto, funcionalidade e integração entre os moradores.

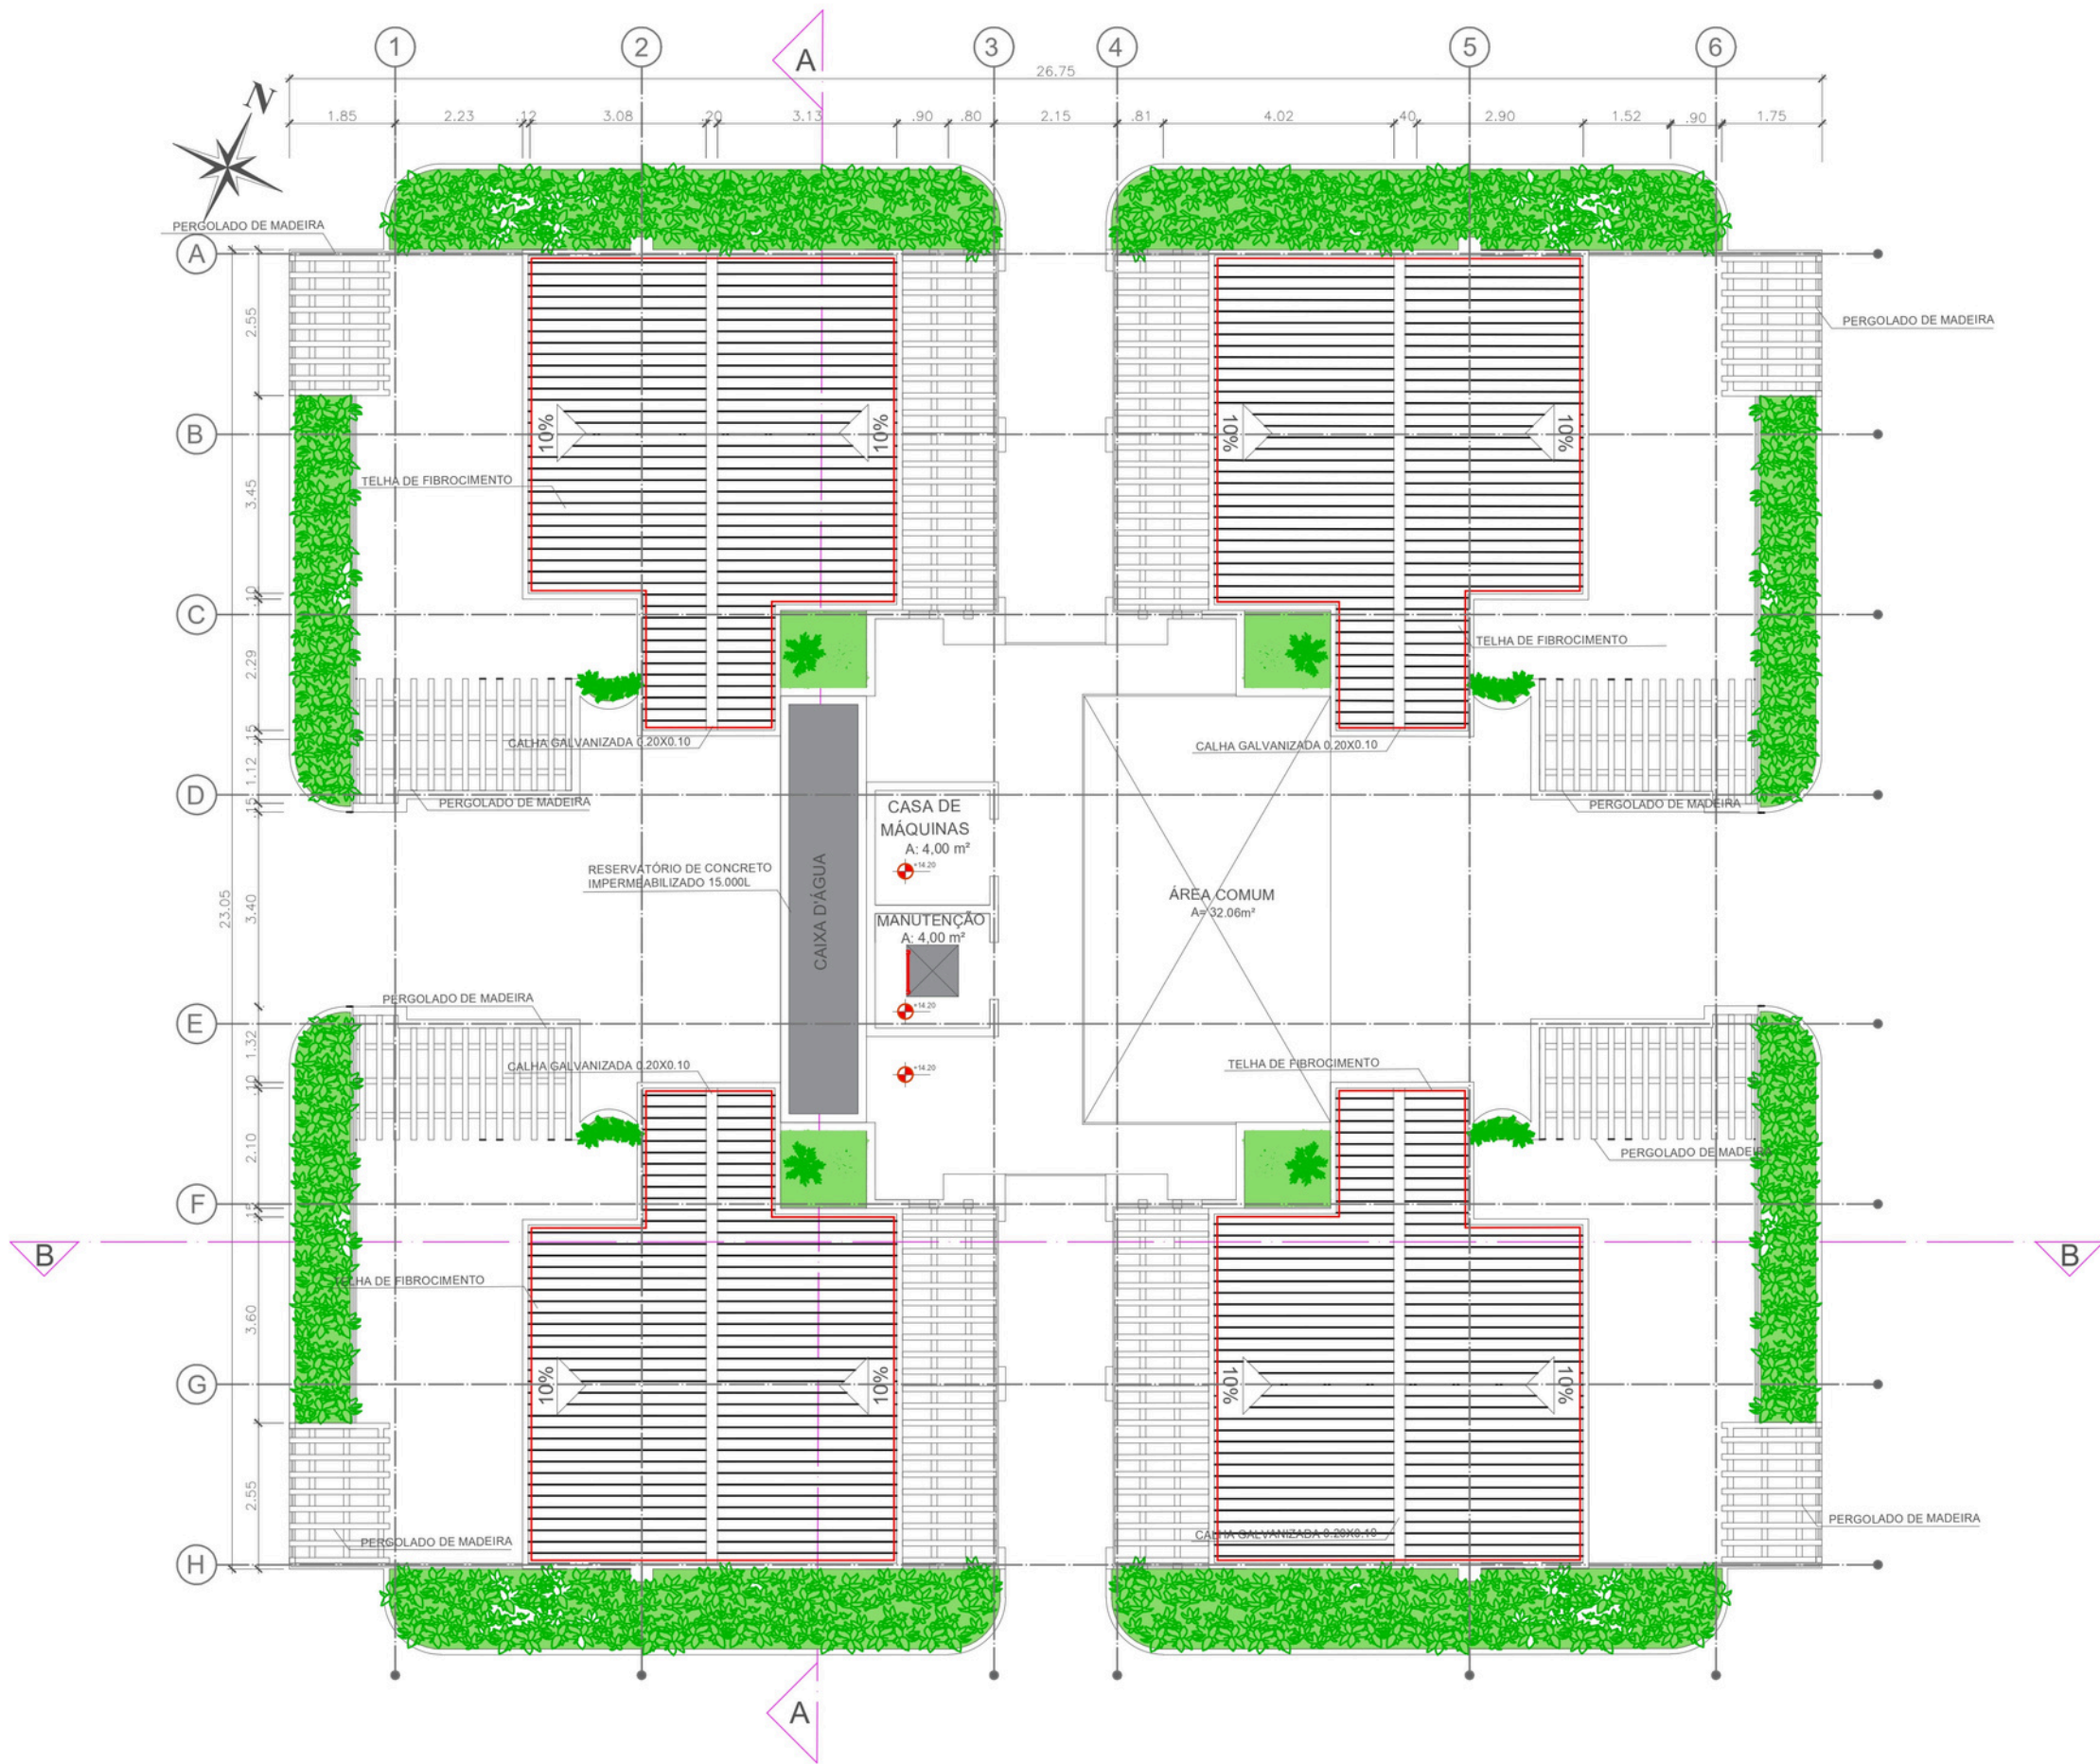

9

COBERTURA - TÉCNICO

ESCALA 1/125

ÍNDICES DA CONSTRUÇÃO

Taxa de Ocupação: 22%
Área Construída: 1.113,91m²
Área do Terreno: 4.913,79m²
Área por Edificação: 466,09m²
Área do Apartamento: 91,82m²

ÍNDICES URBANÍSTICOS

Área: 4.913,79m²
Coeficiente de aproveitamento: 4 - Decreto 13.074
Potencial construtivo: 19.655,16m²
Taxa de ocupação: 70% - Decreto 1412 -1977
Afastamento Frontal: 3,00m
Afastamento Lateral: 1,50m Zona: ZH1

PROJETO: PROJETO DE ARQUITETURA III
ESTUDO DE IMPLANTAÇÃO

ALUNAS: IASMIN GALVÃO E LETÍCIA MARTINS

MATRÍCULAS: 2023121337 e 2023121779



PRANCHA:


ESCALA:
1/125

DESENHO:
09/12


DATA:
03/06/2025

09/12

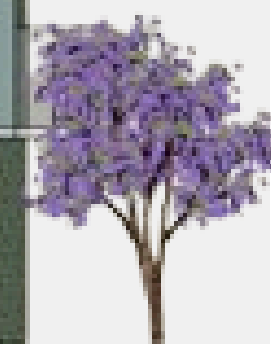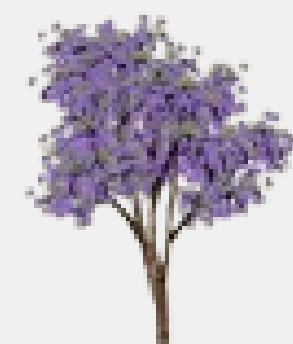

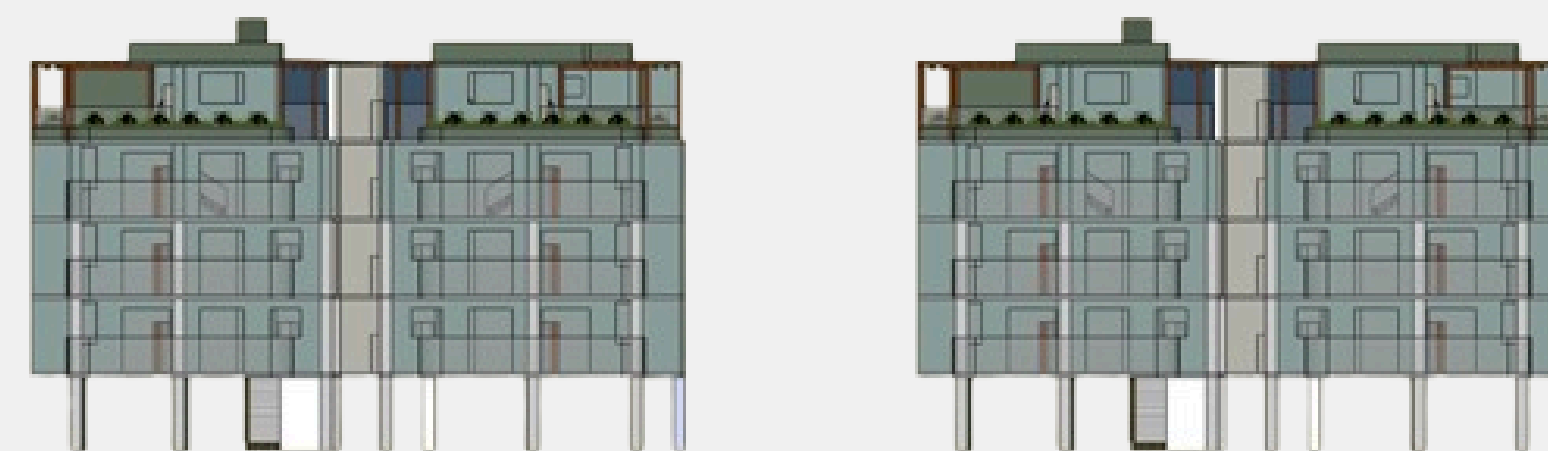

PERFIL ESQUEMÁTICO

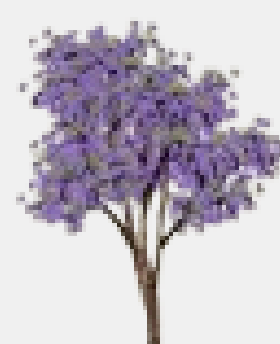



12

RENDERIZAÇÃO AI
SEM ESCALA



